

JAM

ESTADO ACTUAL · PLANTA
DISTRIBUCIÓN

PROYECTO DE REFORMA

REFORMA INTERIOR
VIVIENDA EN EDIFICIO PLURIFAMILIAR


calle Juan Antonio Mayans, 11, 2b

PROMOTOR

Pilar Bravo
Salavador Jordá

ARQUITECTO

Belén Jordá Seguí · no. COACV 15032

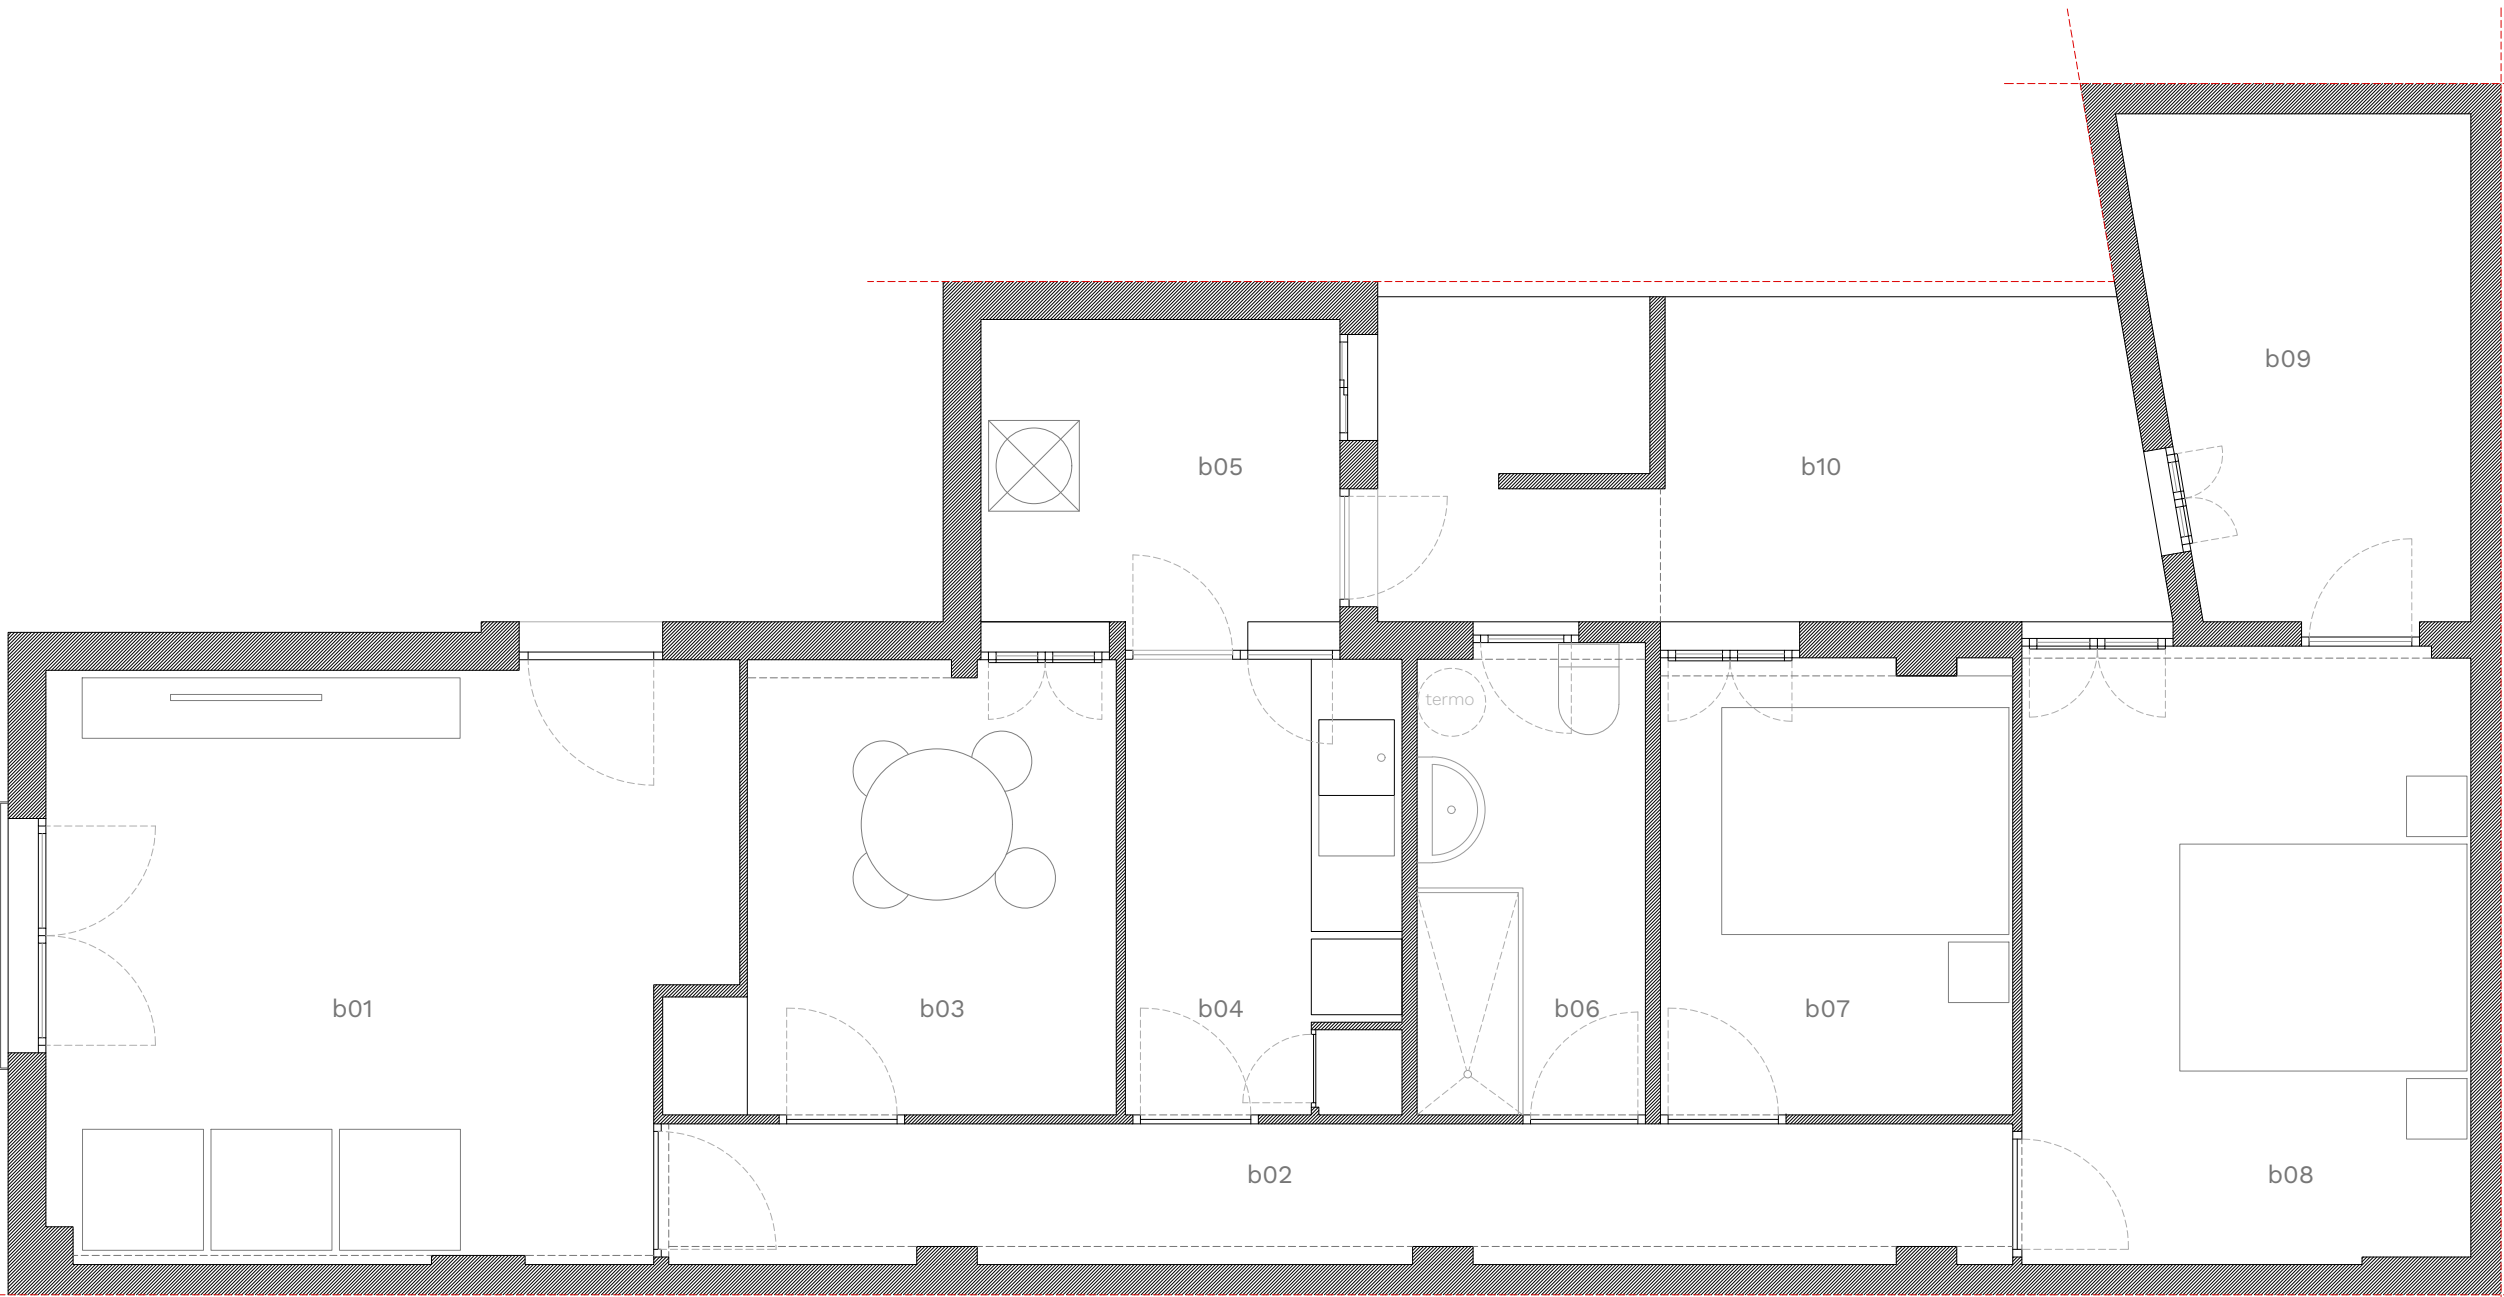



JAM

ESTADO ACTUAL · PLANTA
COTAS Y SUPERFICIES

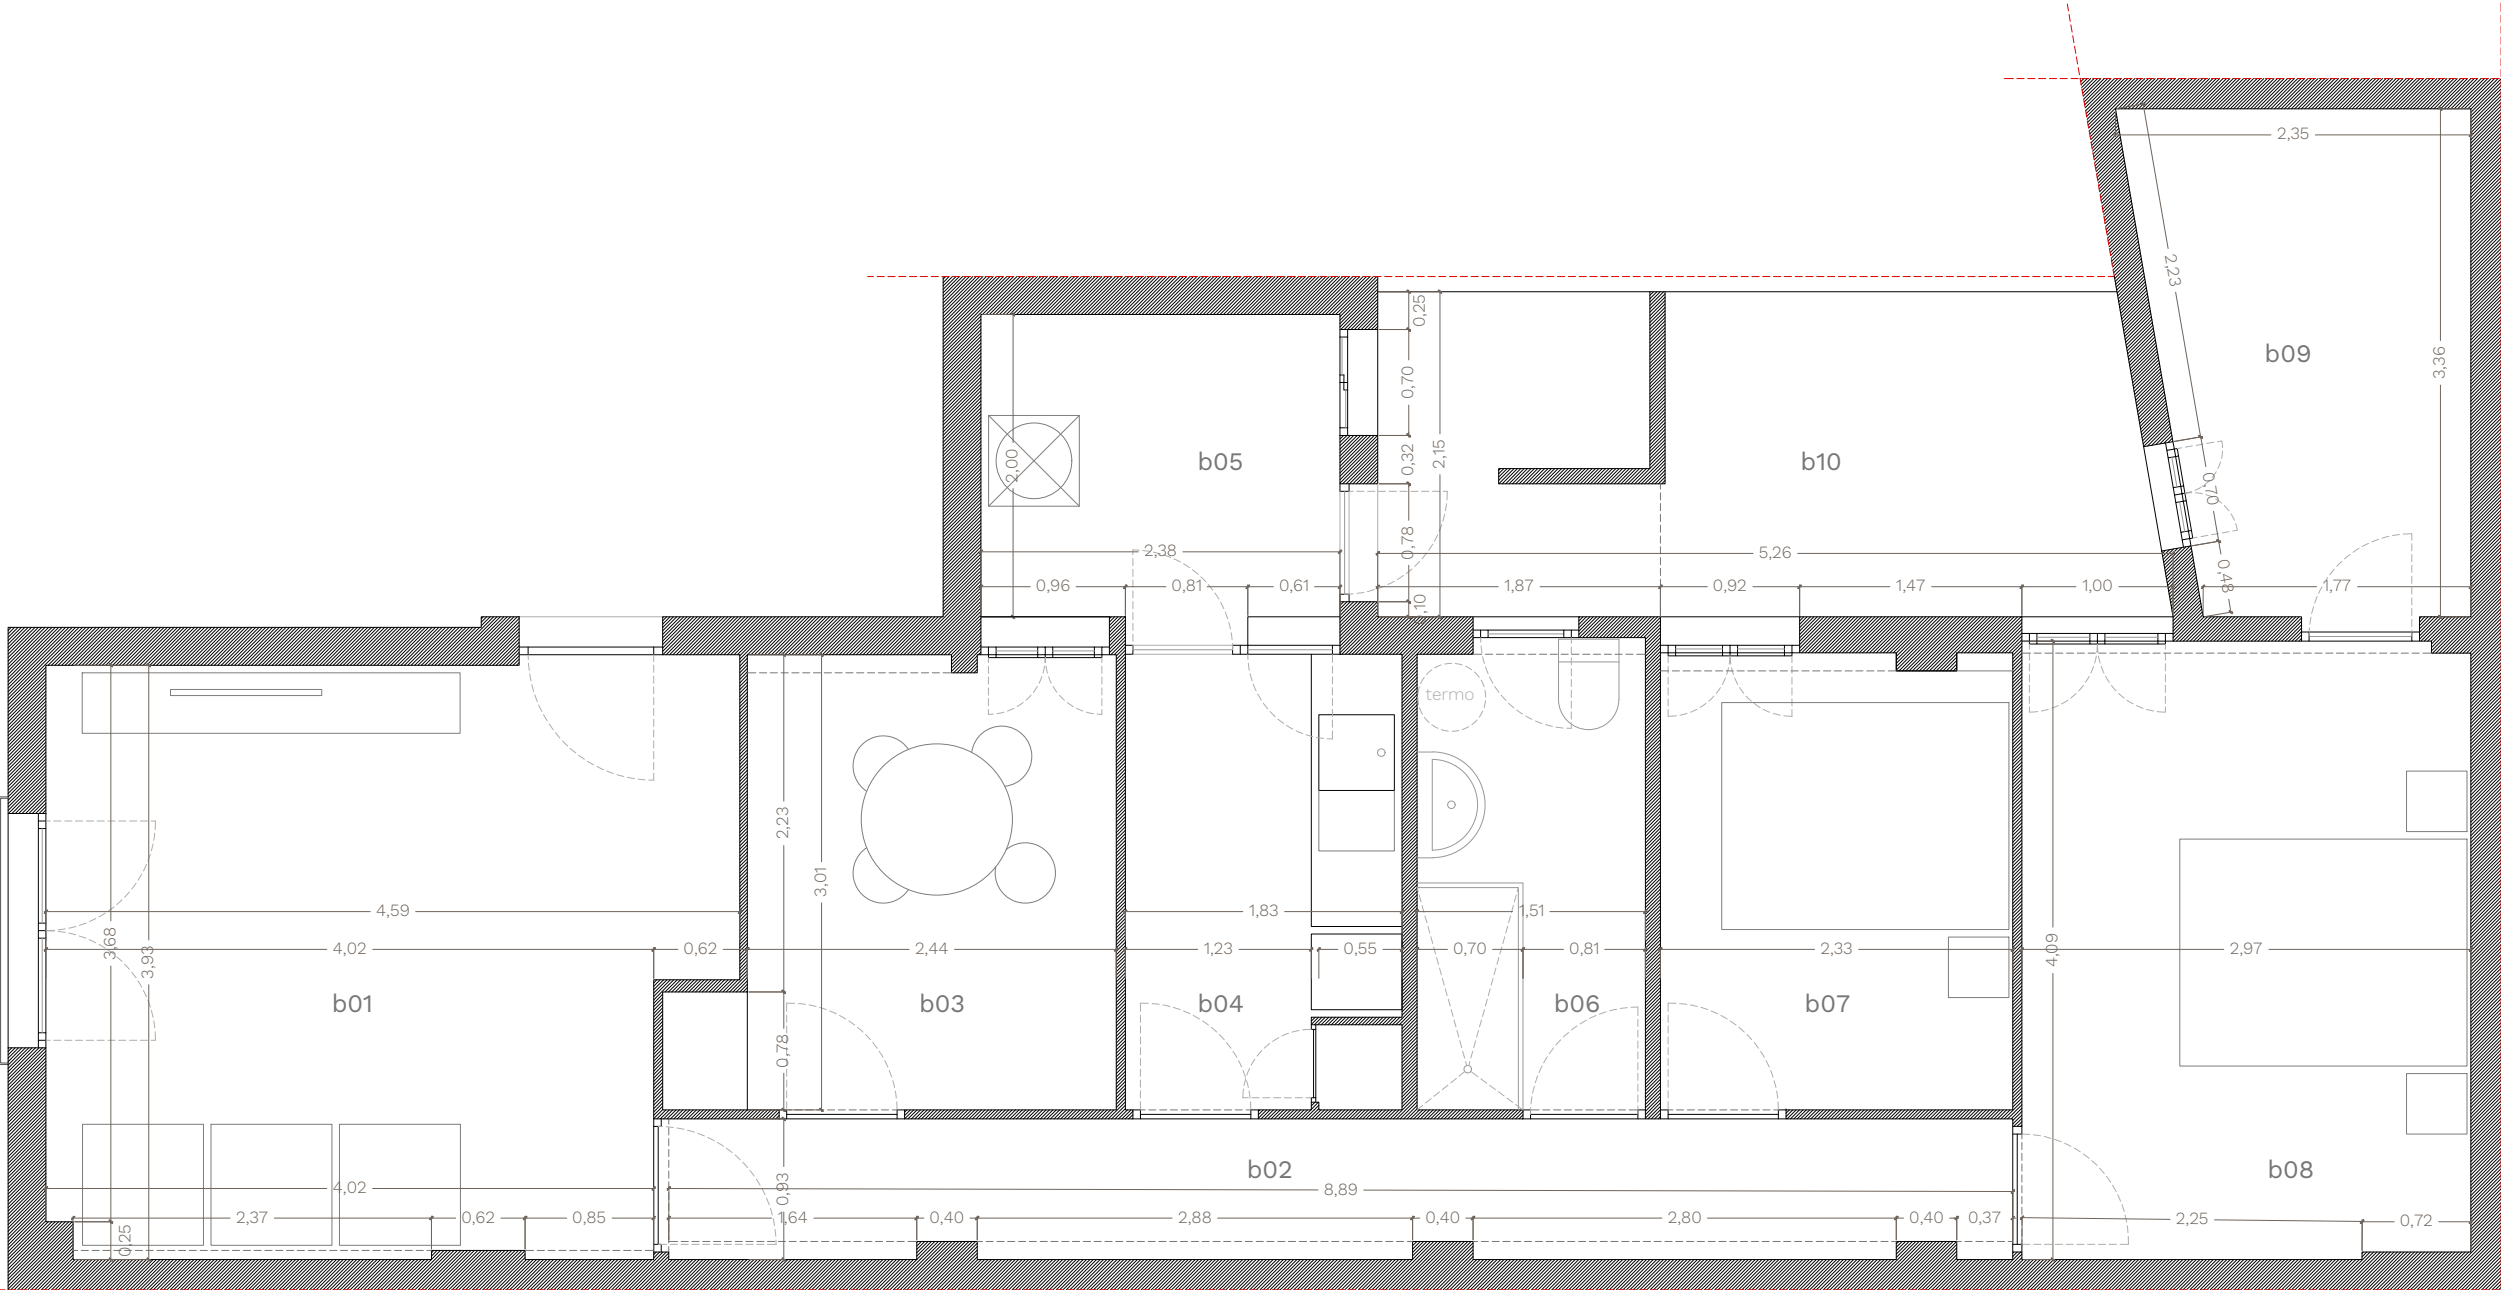


tabla de superficies útiles

ph	planta baja	s. útil	s. const.	s. comput
b01	Salón	17,00	19,72	19,72
b02	Pasillo	8,18	9,32	9,32
b03	Comedor	7,78	8,99	8,99
b04	Cocina	5,24	6,40	6,40
b05	Lavadero	4,90	6,18	6,18
b06	Baño	4,69	5,34	5,34
b07	Habitación 01	7,00	7,83	7,83
b08	Habitación 02	12,09	13,35	13,35
b09	Vestidor	6,98	8,19	8,19
b10	Patio	10,91	10,91	10,91
Total m²		73,86	85,42	85,42

PROYECTO DE REFORMA

REFORMA INTERIOR
VIVIENDA EN EDIFICIO PLURIFAMILIAR


calle Juan Antonio Mayans, 11, 2b


PROMOTOR

Pilar Bravo
Salavador Jordá

ARQUITECTO

Belén Jordá Seguí · no. COACV 15032

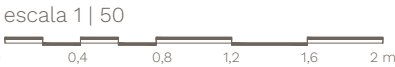

 

JAM

ESTADO REFORMADO · PLANTA
DISTRIBUCIÓN

PROYECTO DE REFORMA

REFORMA INTERIOR
VIVIENDA EN EDIFICIO PLURIFAMILIAR


calle Juan Antonio Mayans, 11, 2b

PROMOTOR

Pilar Bravo
Salavador Jordá

ARQUITECTO

Belén Jordá Seguí · no. COACV 15032

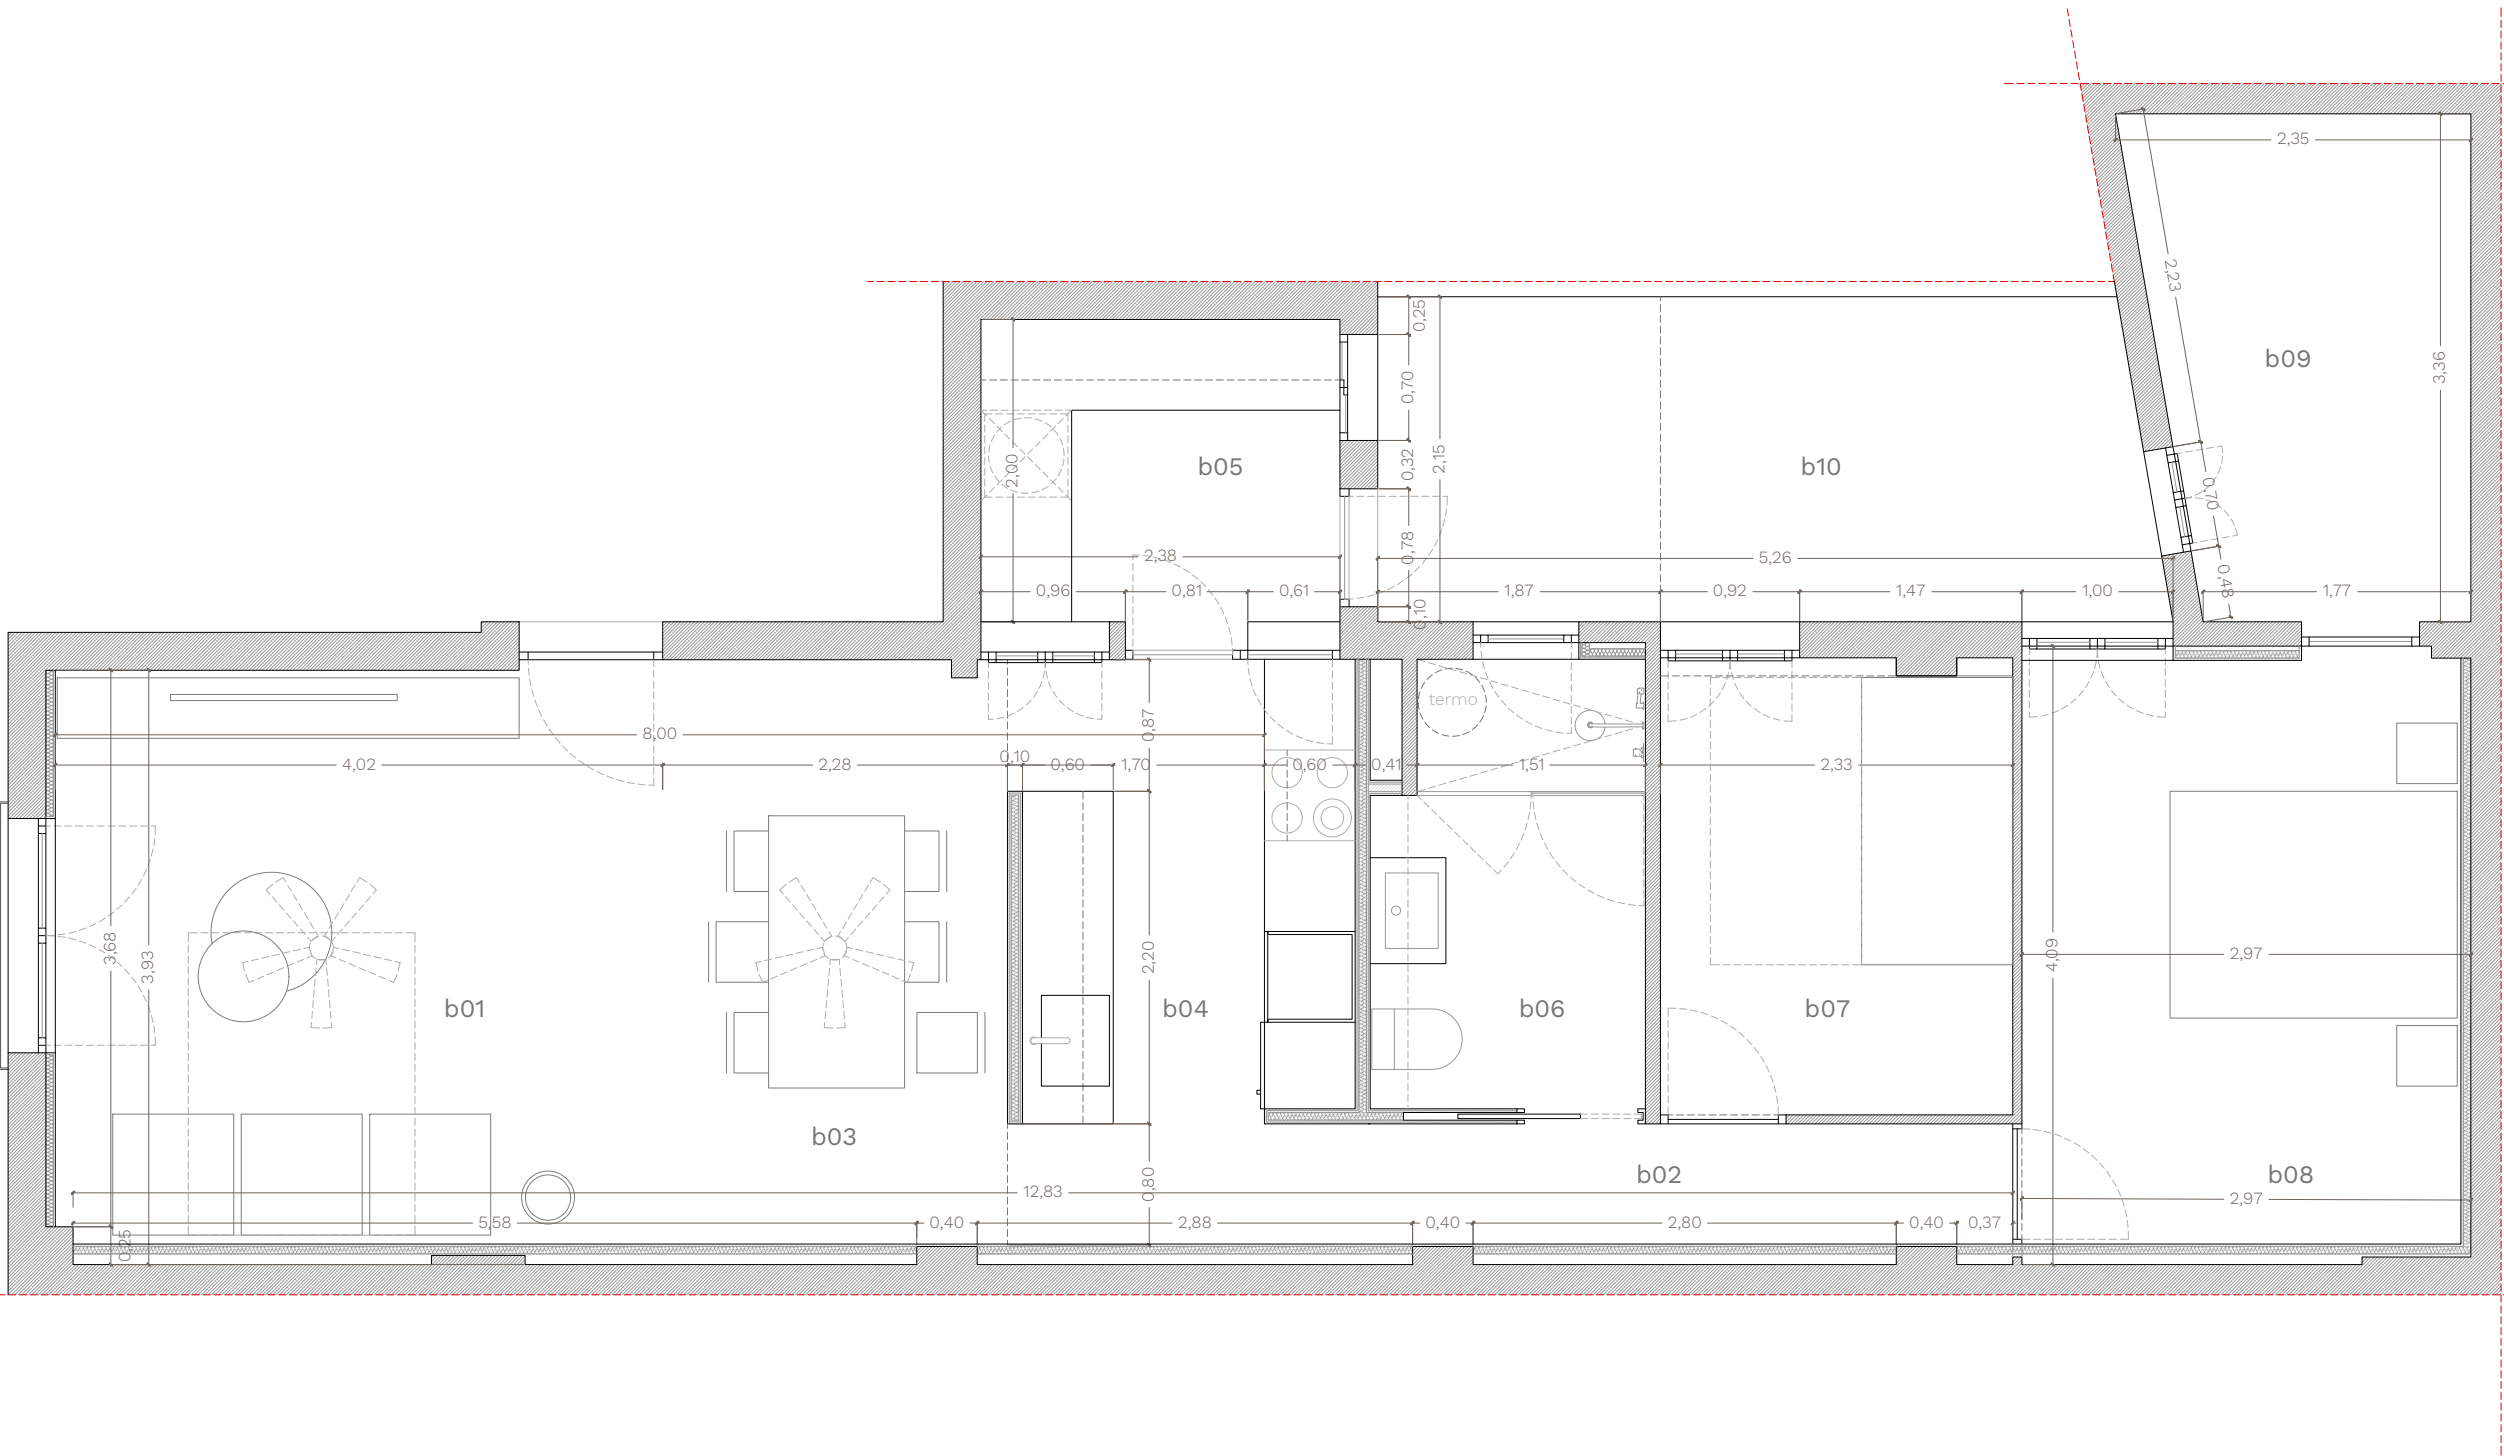

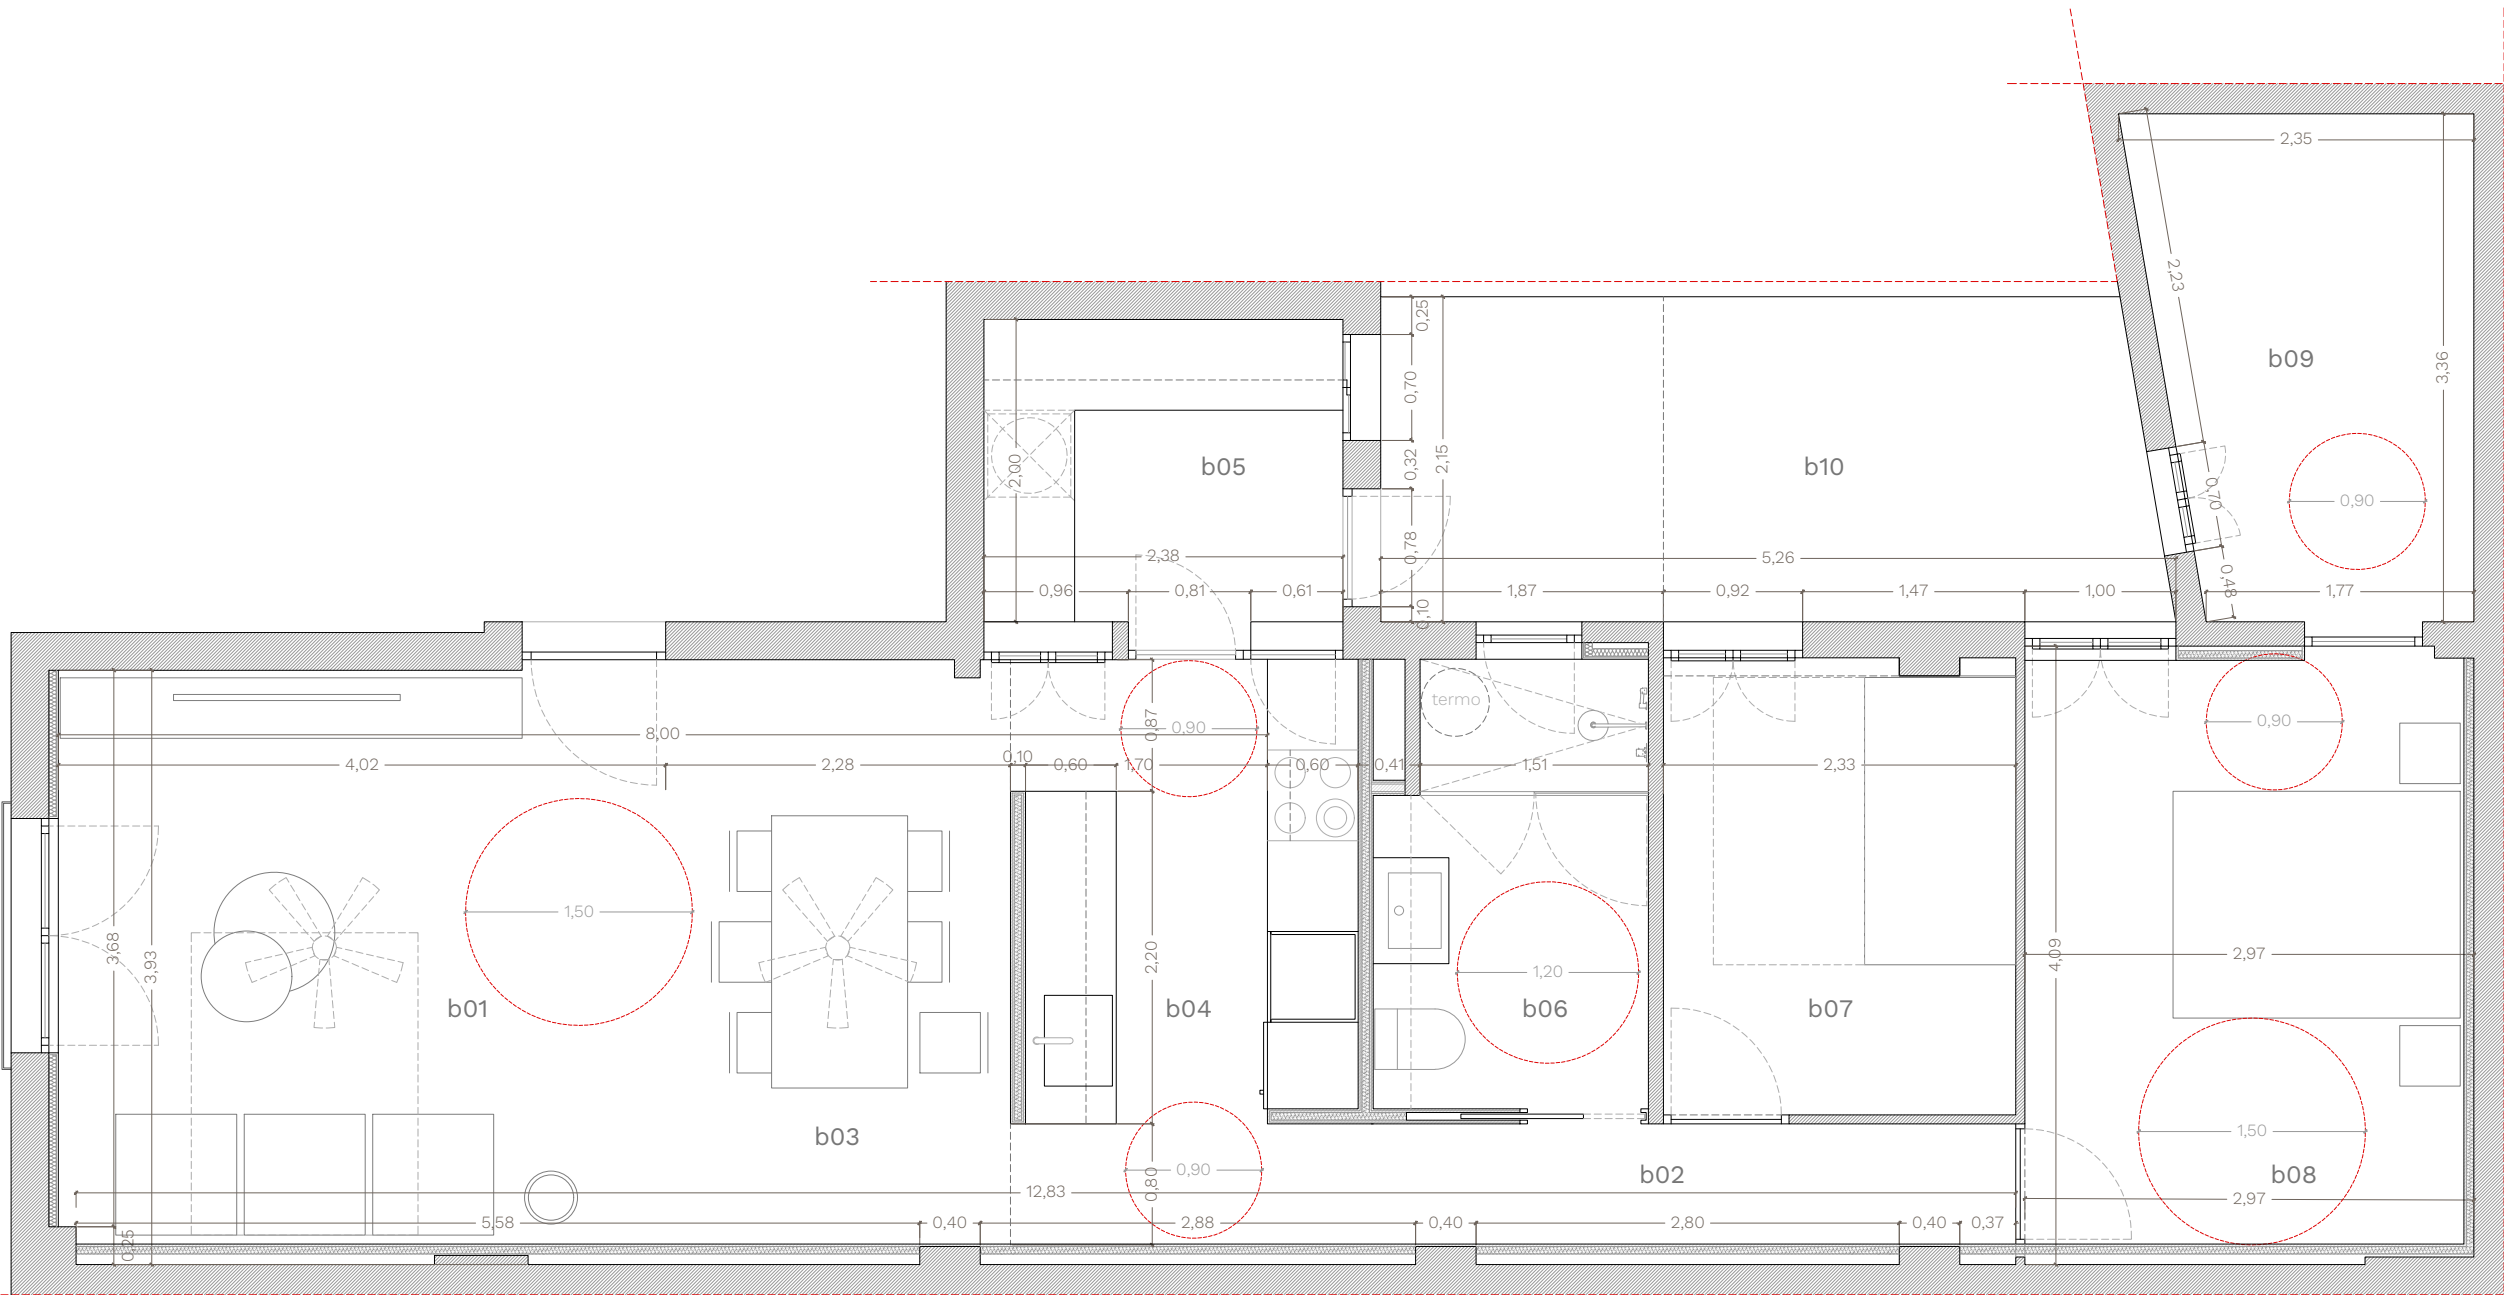


tabla de superficies útiles

pb	planta baja	s. útil	s. const.	s. comput
b01+b03	Salón-comedor	24,74	28,97	28,97
b02	Pasillo	3,96	5,10	5,10
b04	Cocina	7,97	9,28	9,28
b05	Lavadero	4,90	6,18	6,18
b06	Baño	5,20	6,37	6,37
b07	Habitación 01	6,99	7,93	7,93
b08	Habitación 02	12,08	13,35	13,35
b09	Vestidor	6,98	8,19	8,19
b10	Patio	10,91	10,91	10,91
Total m²		72,83	85,37	85,37



JAM

ESTADO REFORMADO · PLANTA

COTAS Y SUPERFICIES 01

PROYECTO DE REFORMA

REFORMA INTERIOR
VIVIENDA EN EDIFICIO PLURIFAMILIAR



calle Juan Antonio Mayans, 11, 2b

PROMOTOR

Pilar Bravo
Salavador Jordá

ARQUITECTO


Belén Jordá Seguí · no. COACV 15032

 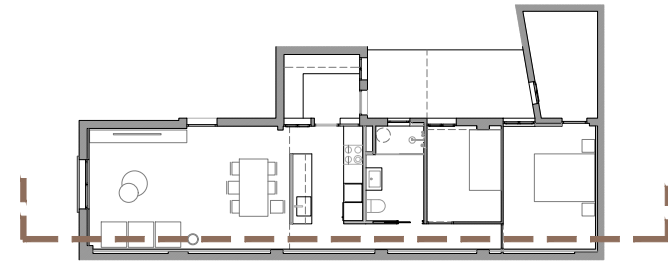

JAM

ESTADO REFORMADO • SECCIÓN

SECCIÓN LONGITUDINAL

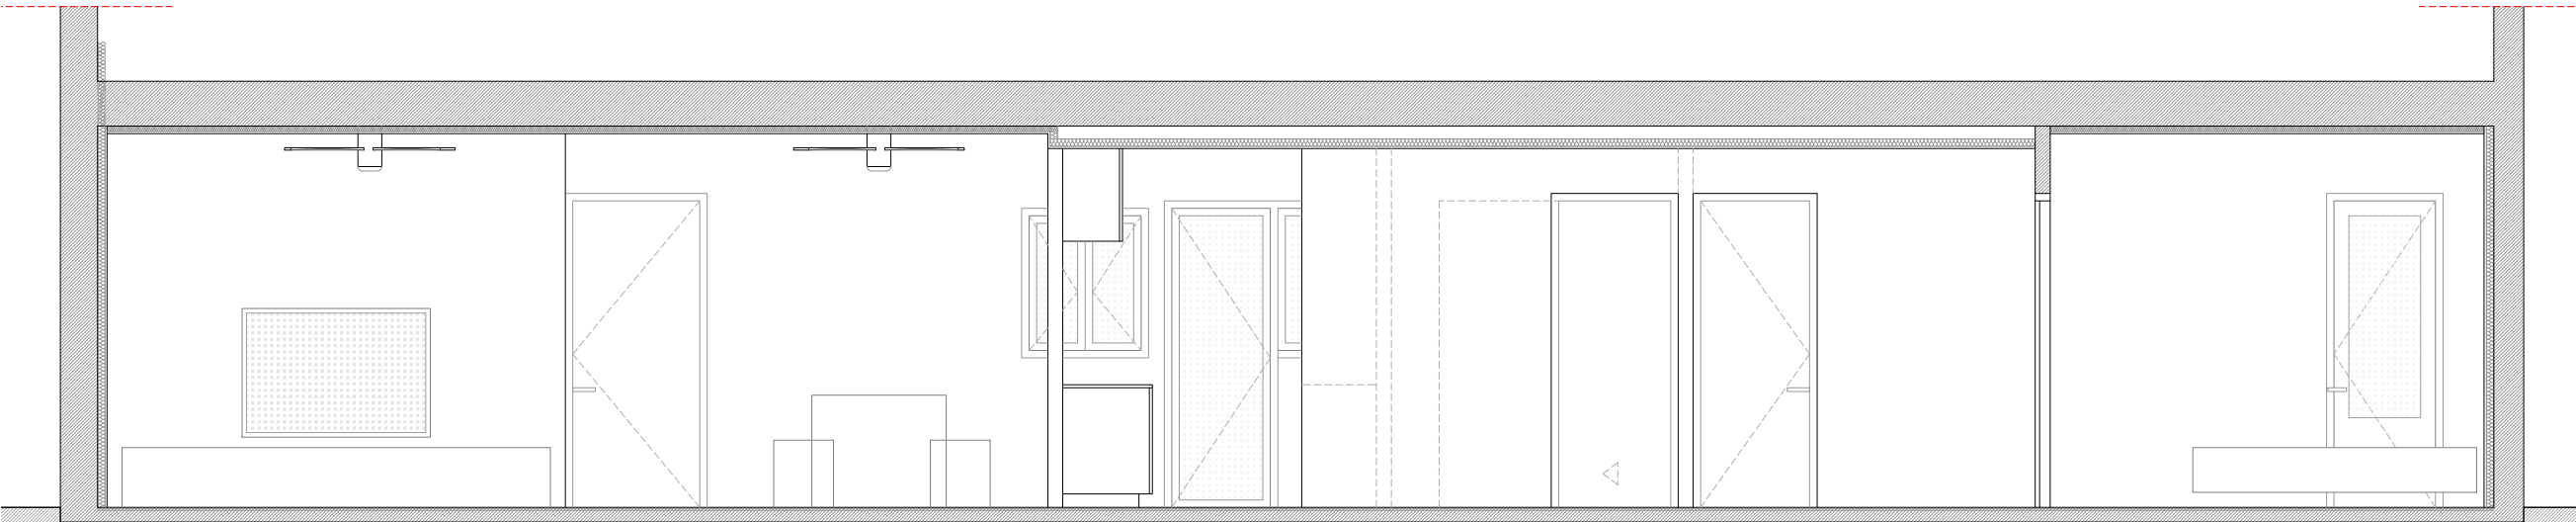

PROYECTO DE REFORMA

REFORMA INTERIOR
VIVIENDA EN EDIFICIO PLURIFAMILIAR

calle Juan Antonio Mayans, 11, 2b

PROMOTOR

Pilar Bravo
Salavador Jordá

ARQUITECTO

Belén Jordá Seguí · no. COACV 15032

