



PIB

e01

ESTADO ACTUAL

PLANTA BAJA
DISTRIBUCIÓN

VIVIENDA UNIFAMILIAR AISLADA
PROYECTO DE REFORMA Y
REHABILITACIÓN DE VIVIENDA
UNIFAMILIAR ENTRE MEDIANERAS

calle Bernardino Pellarés, 37
46712, Piles, Valencia


PROMOTORES

Marta Server
--

ARQUITECTA

Belén Jordá Seguí · no. COACV 15032



 

PIB

e02

ESTADO ACTUAL


PLANTA PRIMERA
DISTRIBUCIÓN


VIVIENDA UNIFAMILIAR AISLADA
PROYECTO DE REFORMA Y
REHABILITACIÓN DE VIVIENDA
UNIFAMILIAR ENTRE MEDIANERAS

calle Bernardino Pallarés, 37
46712, Piles, Valencia

PROMOTORES
Marta Server
--

ARQUITECTA
Belén Jordá Seguí · no. COACV 15032

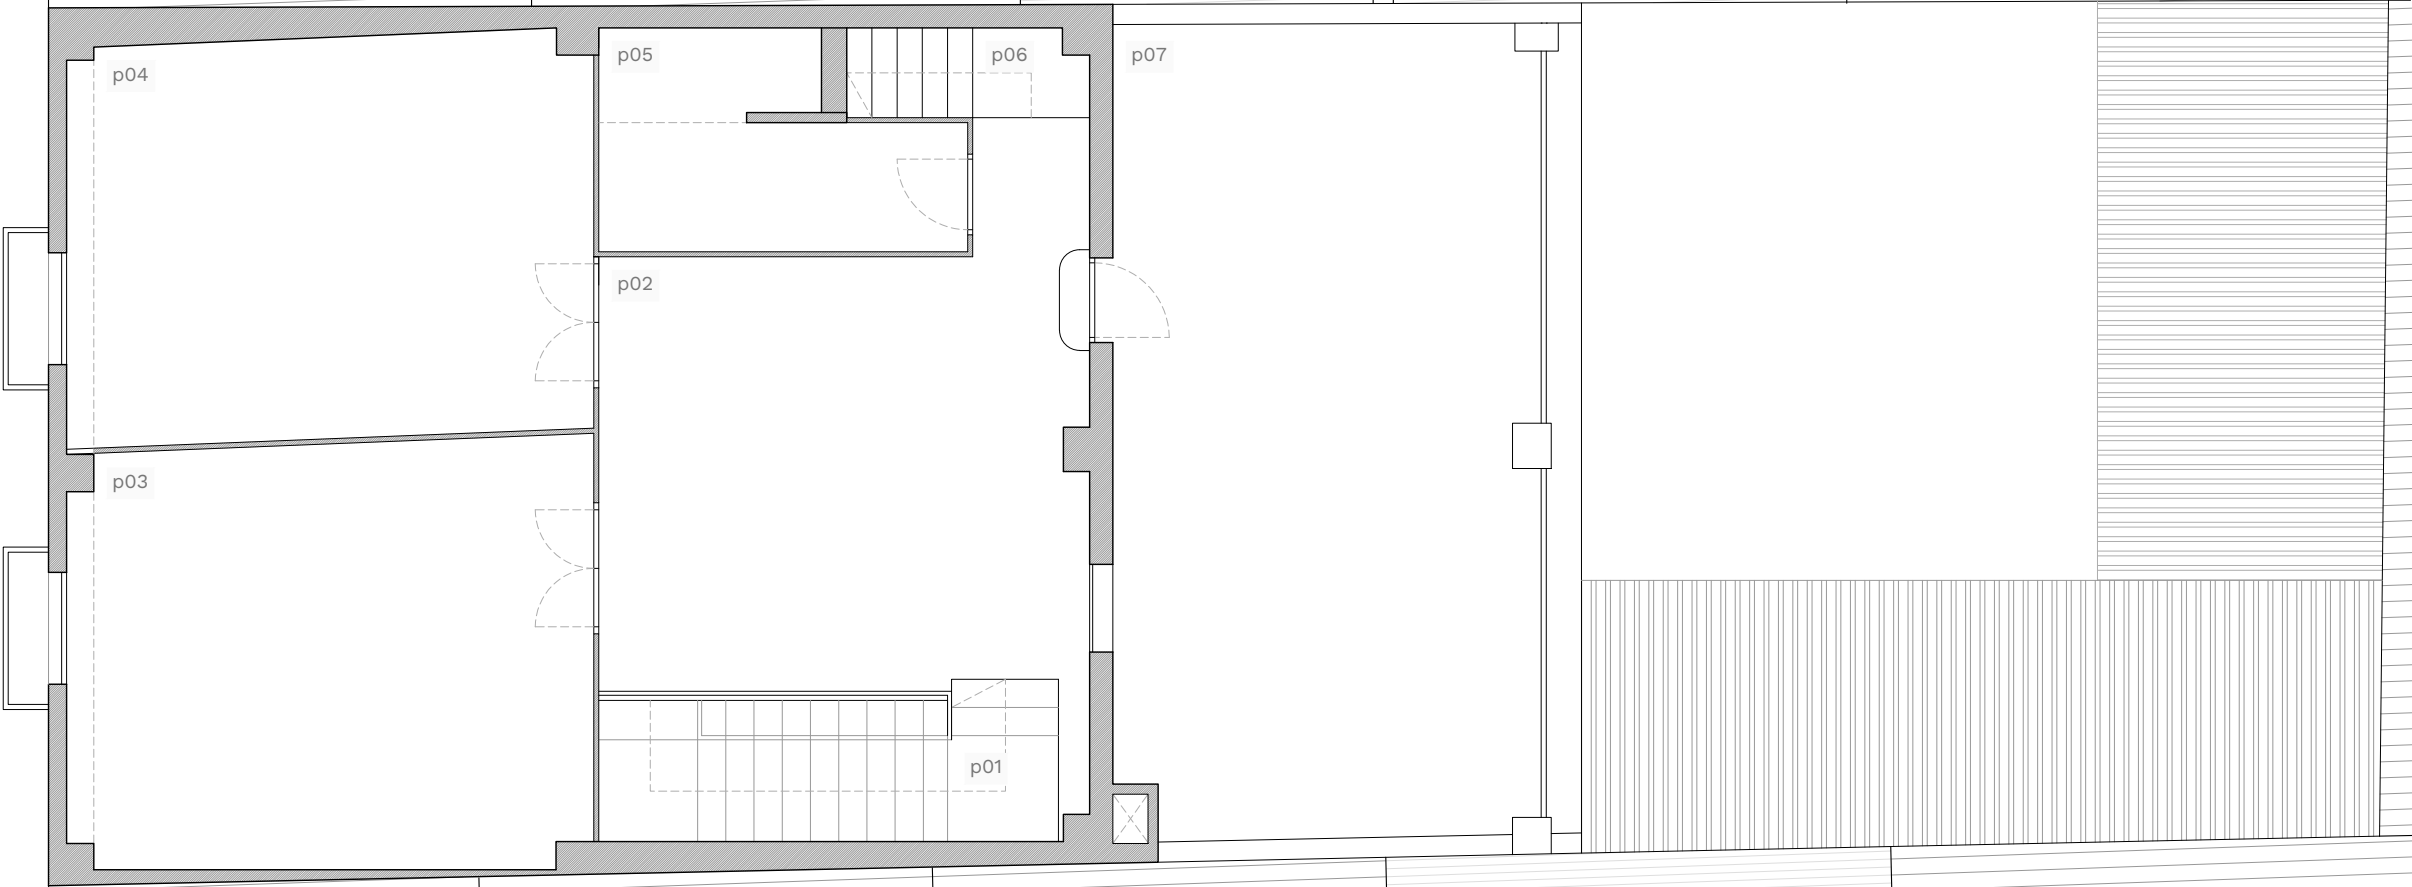

 

PIB

p01

PLANTAS


PLANTA BAJA
DISTRIBUCIÓN


VIVIENDA UNIFAMILIAR AISLADA
PROYECTO DE REFORMA Y
REHABILITACIÓN DE VIVIENDA
UNIFAMILIAR ENTRE MEDIANERAS

calle Bernardino Pellarés, 37
46712, Piles, Valencia

PROMOTORES
Marta Server
--

ARQUITECTA
Belén Jordá Seguí · no. COACV 15032

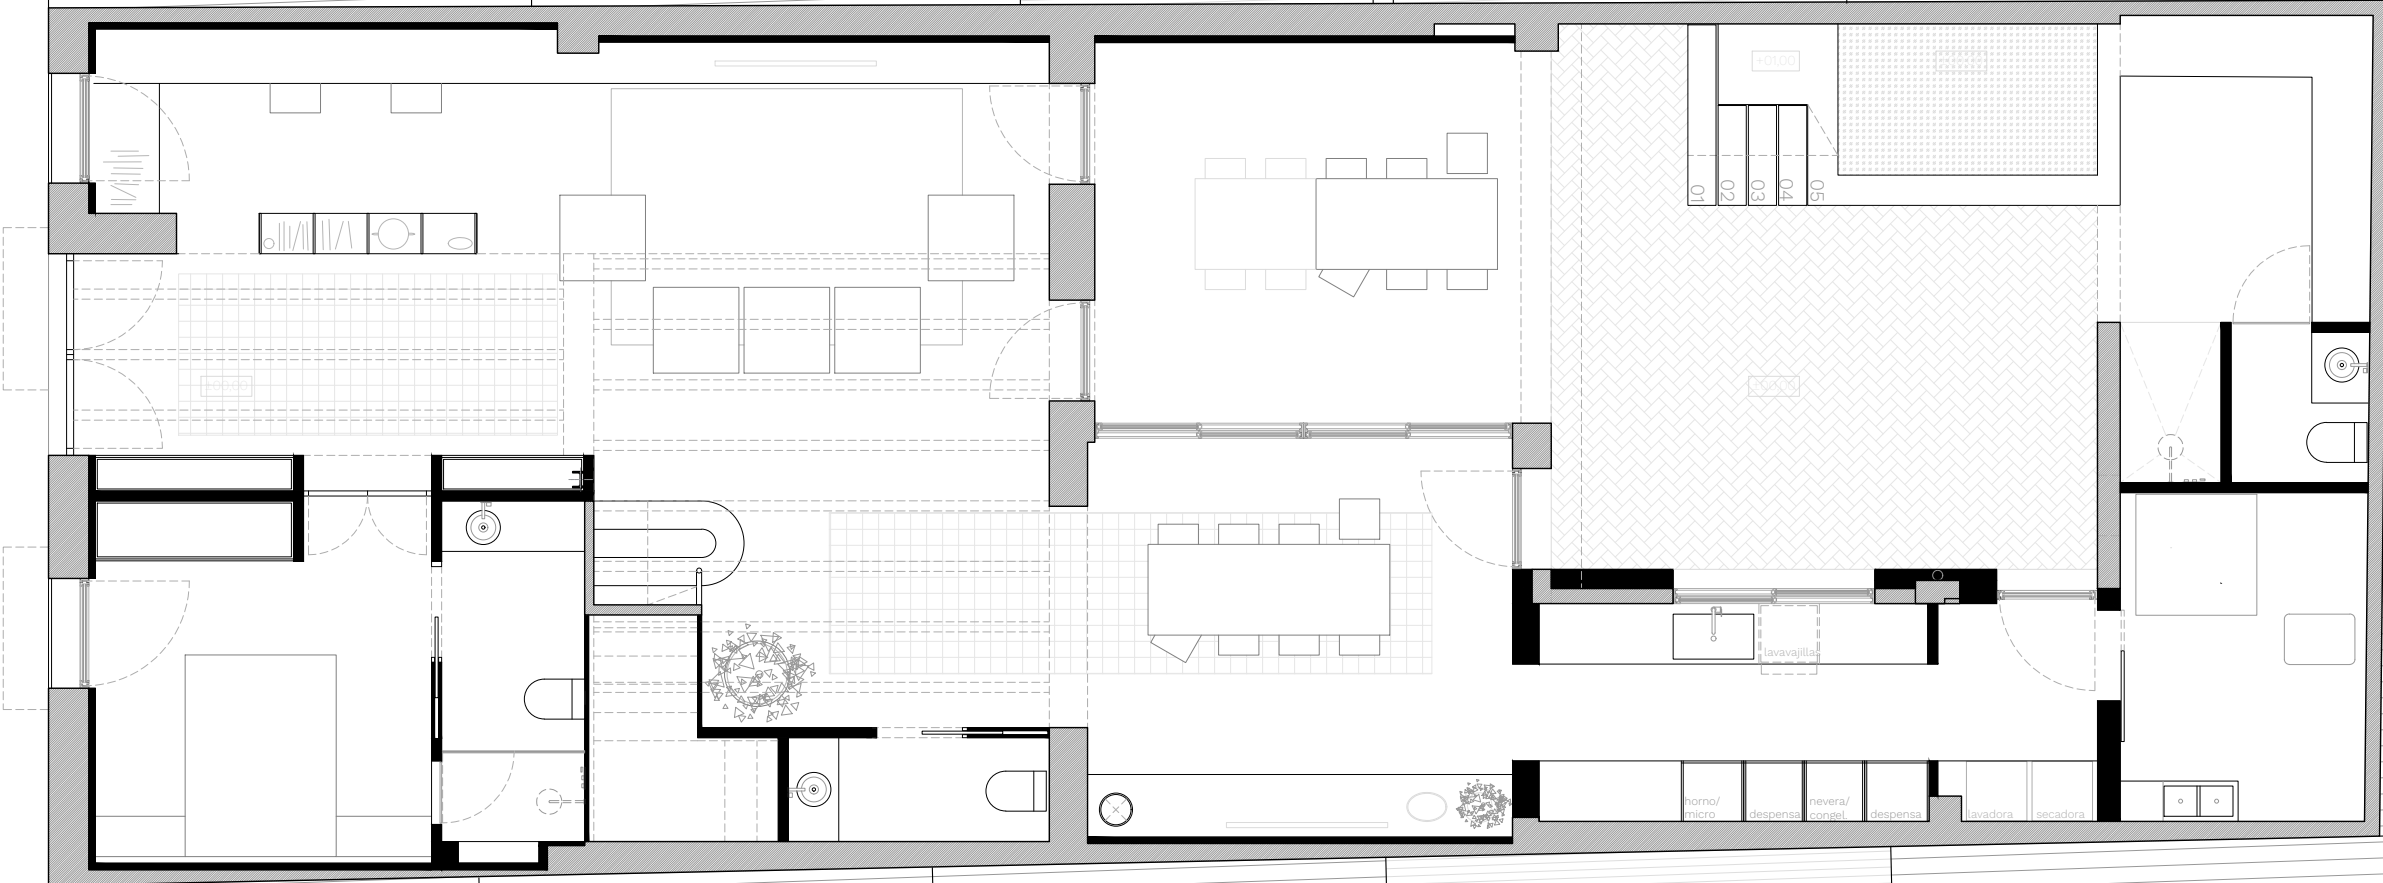

 

PIB

p02

PLANTAS

PLANTA PRIMERA
DISTRIBUCIÓN

VIVIENDA UNIFAMILIAR AISLADA
PROYECTO DE REFORMA Y
REHABILITACIÓN DE VIVIENDA
UNIFAMILIAR ENTRE MEDIANERAS

calle Bernardino Pallarés, 37
46712, Piles, Valencia

PROMOTORES
Marta Server
--

ARQUITECTA
Belén Jordá Seguí · no. COACV 15032

