


VISADO DE COLEGIO OFICIAL DE ARQUITECTOS
DE LA COMUNIDAD VALENCIAN | COACV

TOR

a01

ALZADOS
C. GREGORI MAIANS

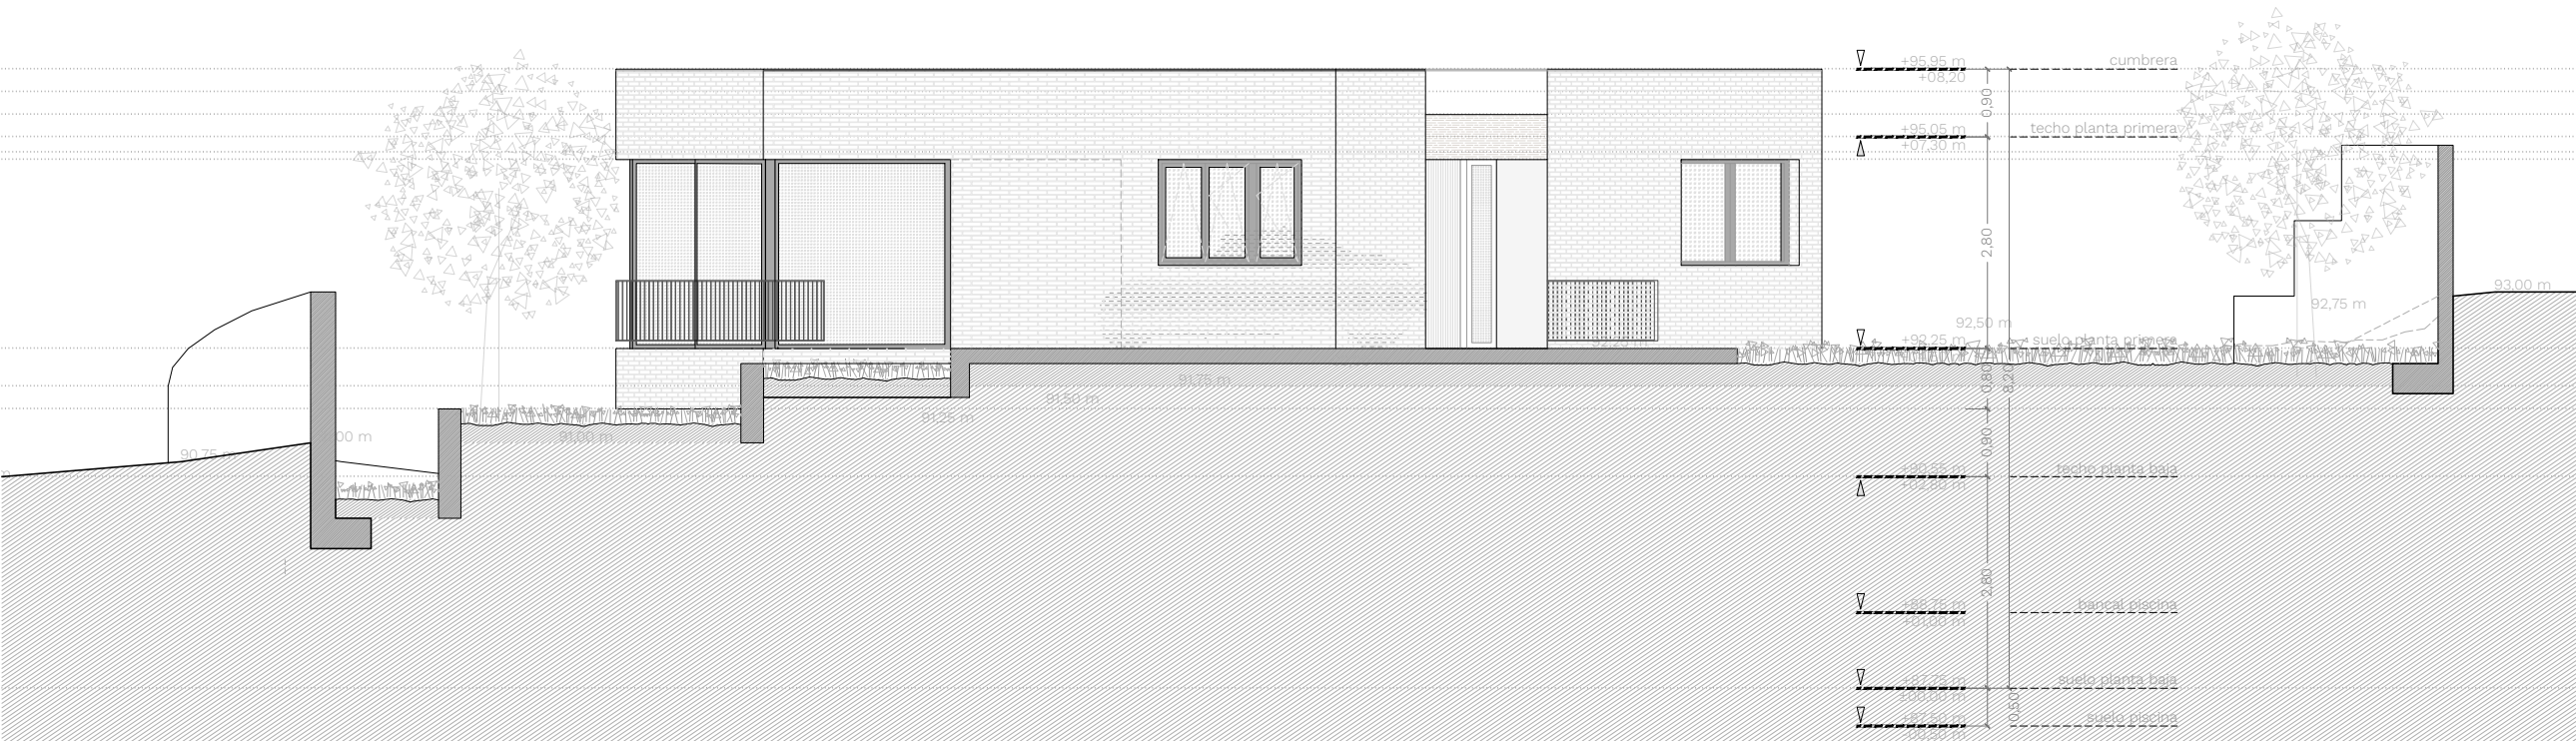

VIVIENDA UNIFAMILIAR AISLADA

PROYECTO BÁSICO
calle Gregori Maïans, 20
46900, Torrent, Valencia

FECHA
JUNIO 2025

PROMOTORES
Ana Isabel Esquivias Maroto
Basilio Herguido Toledo

ARQUITECTA
Belén Jordá Seguí · no. COACV 15032

DISTRITO ARQUITECTURA