




RBR

ci01 · CARPINTERÍAS INTERIORES

LOCALIZADORES

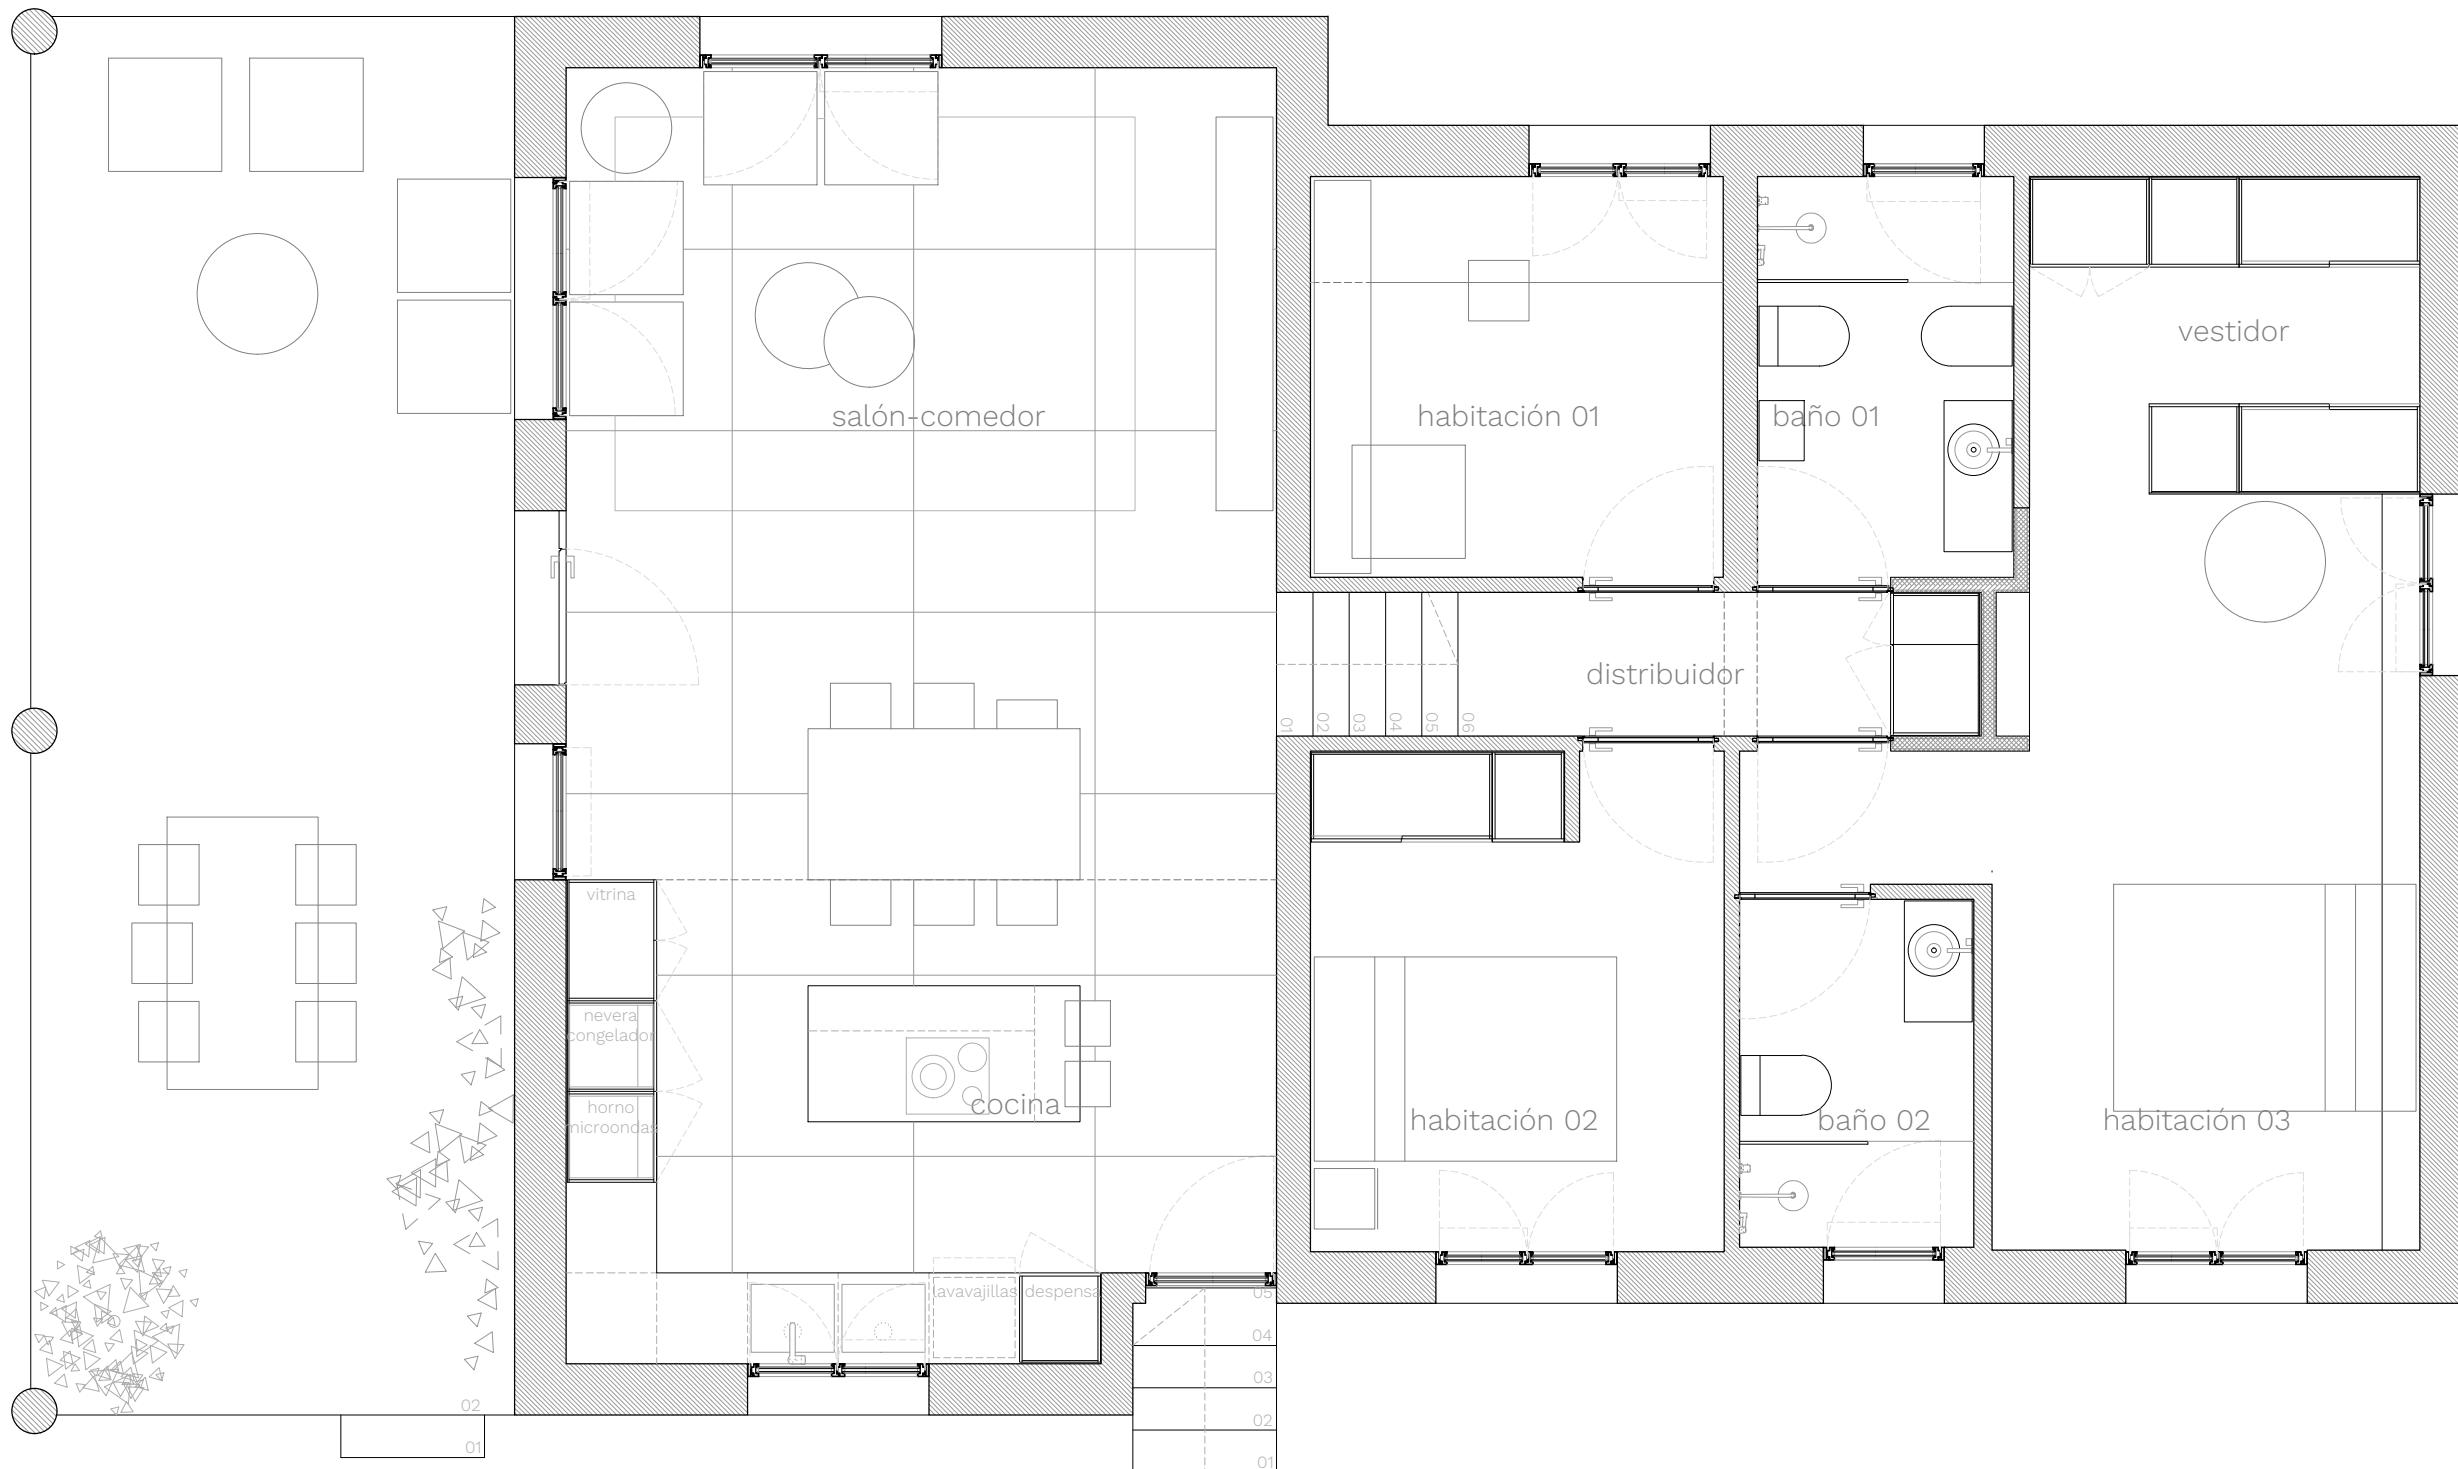

MEMORIA VALORADA

REFORMA INTERIOR
VIVIENDA UNIFAMILIAR AISLADA
calle 103, 33
46182, Riba-Roja del Túria, Valencia

PROMOTOR

Martina Zandara
Mario Martínez Corcoles

ARQUITECTO

Belén Jordá Seguí · no. COACV 15032
calle Azcárraga, 14, 2
46008, València